

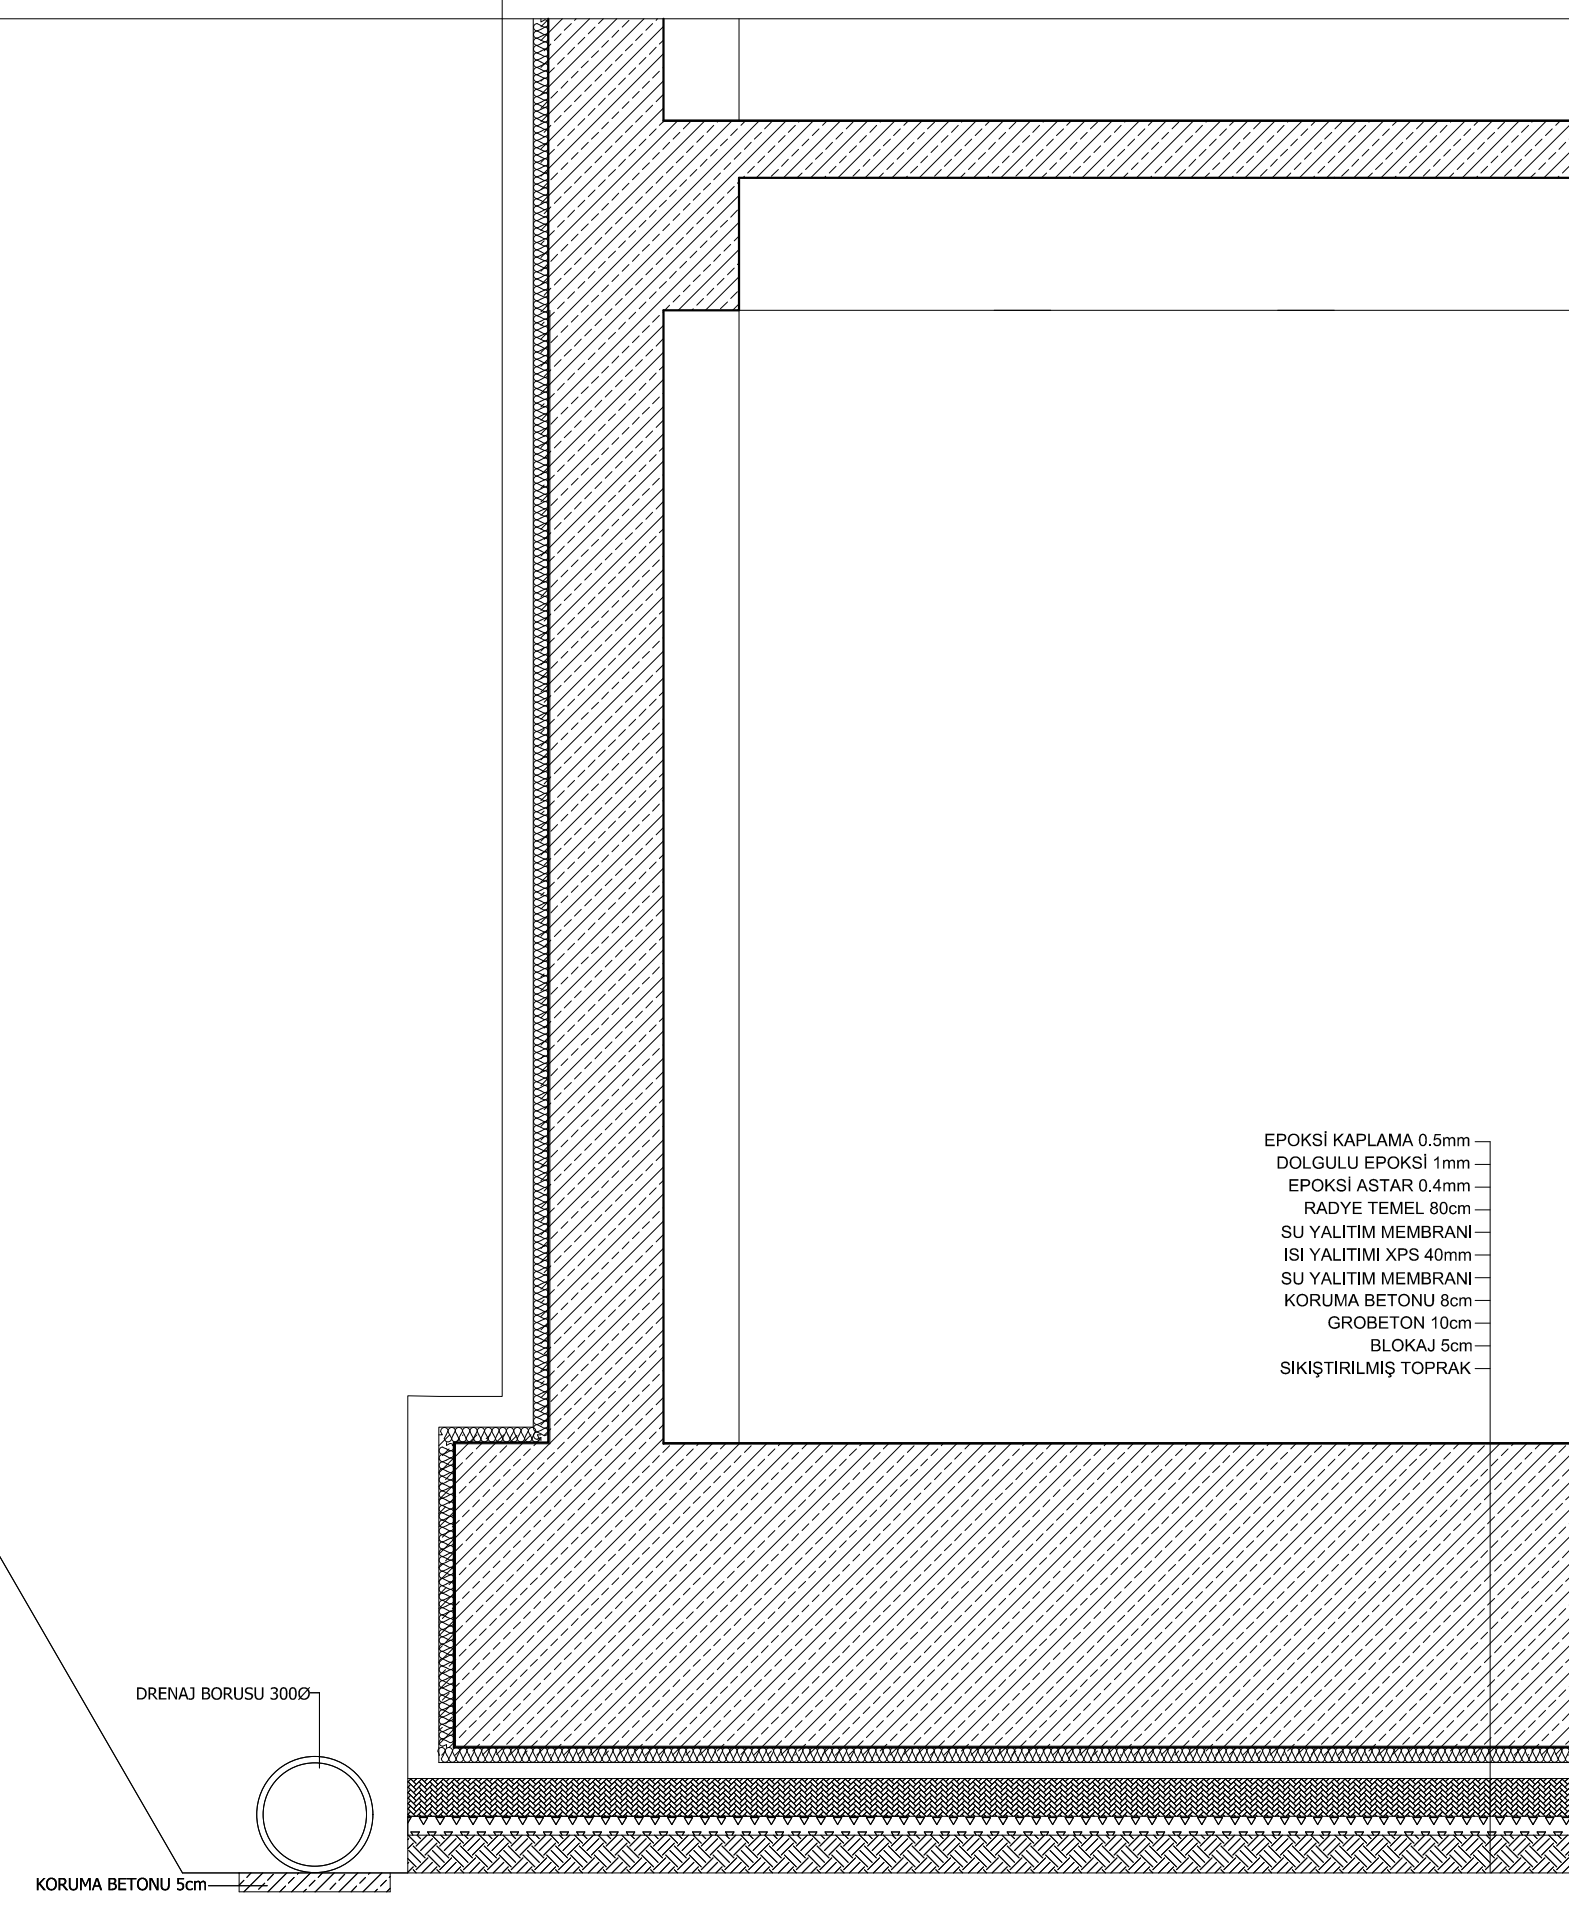


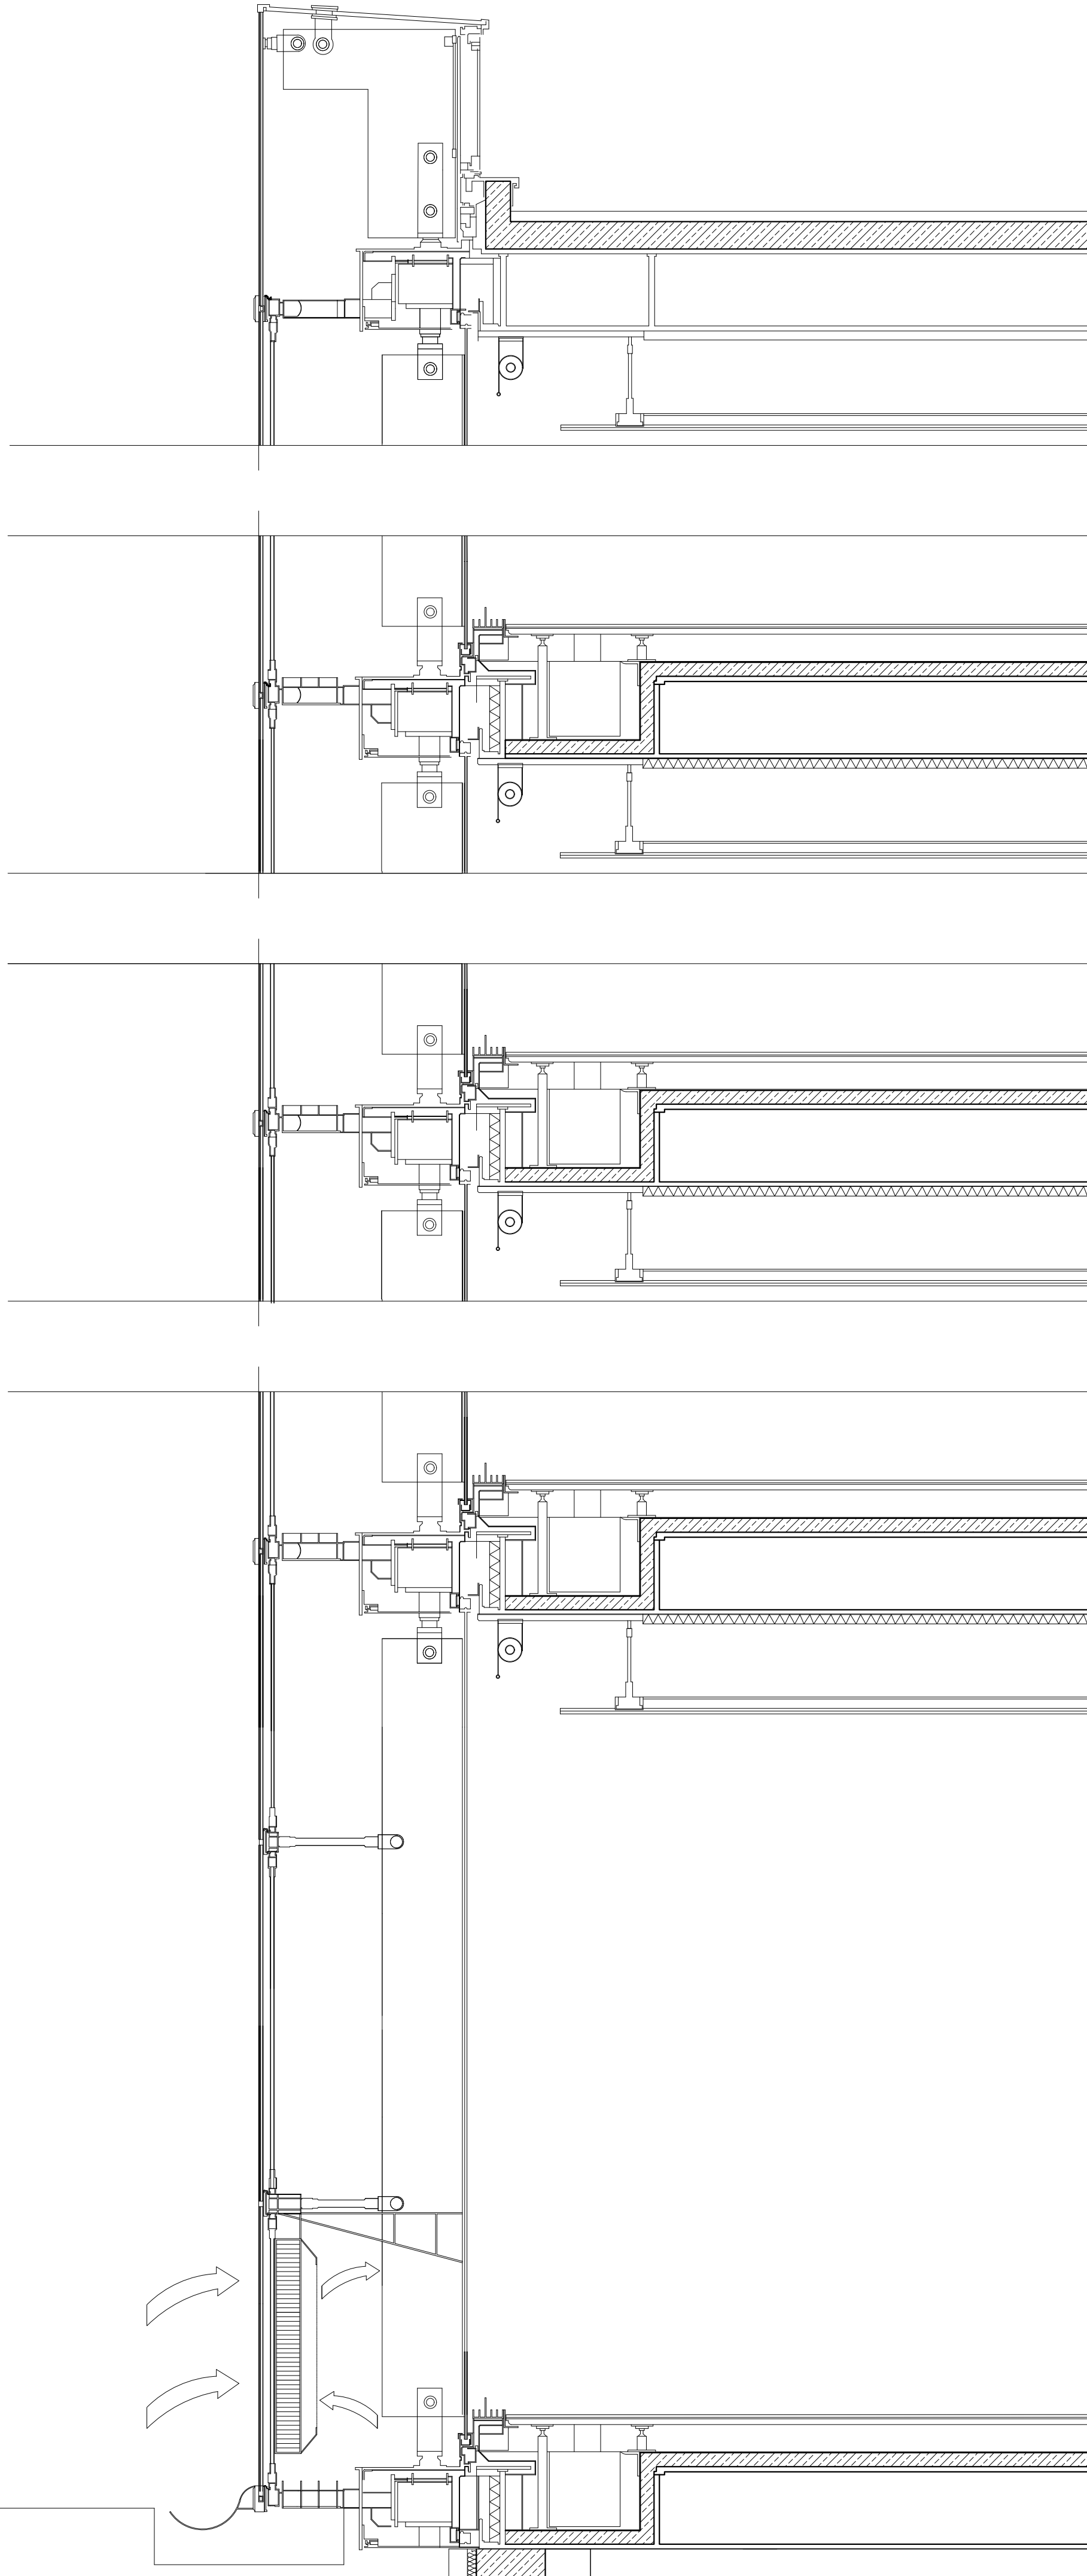


EPOKSİ KAPLAMA 0.5mm
DOĞULU EPOKSİ 1mm
EPOKSİ AÇIK 0.5mm
PAZELİ TİNEL 10mm
SU YALITIM MERMERİ
SU YALITIM 0.5mm
SU YALITIM MERMERİ
KORUMA BETONU 10mm
GROBETON 150mm
BİÇİMLİ
SİKSİTİRLİNG TOPRAK

DEYALİ BORUSU 300mm
KORUMA BETONU 50mm

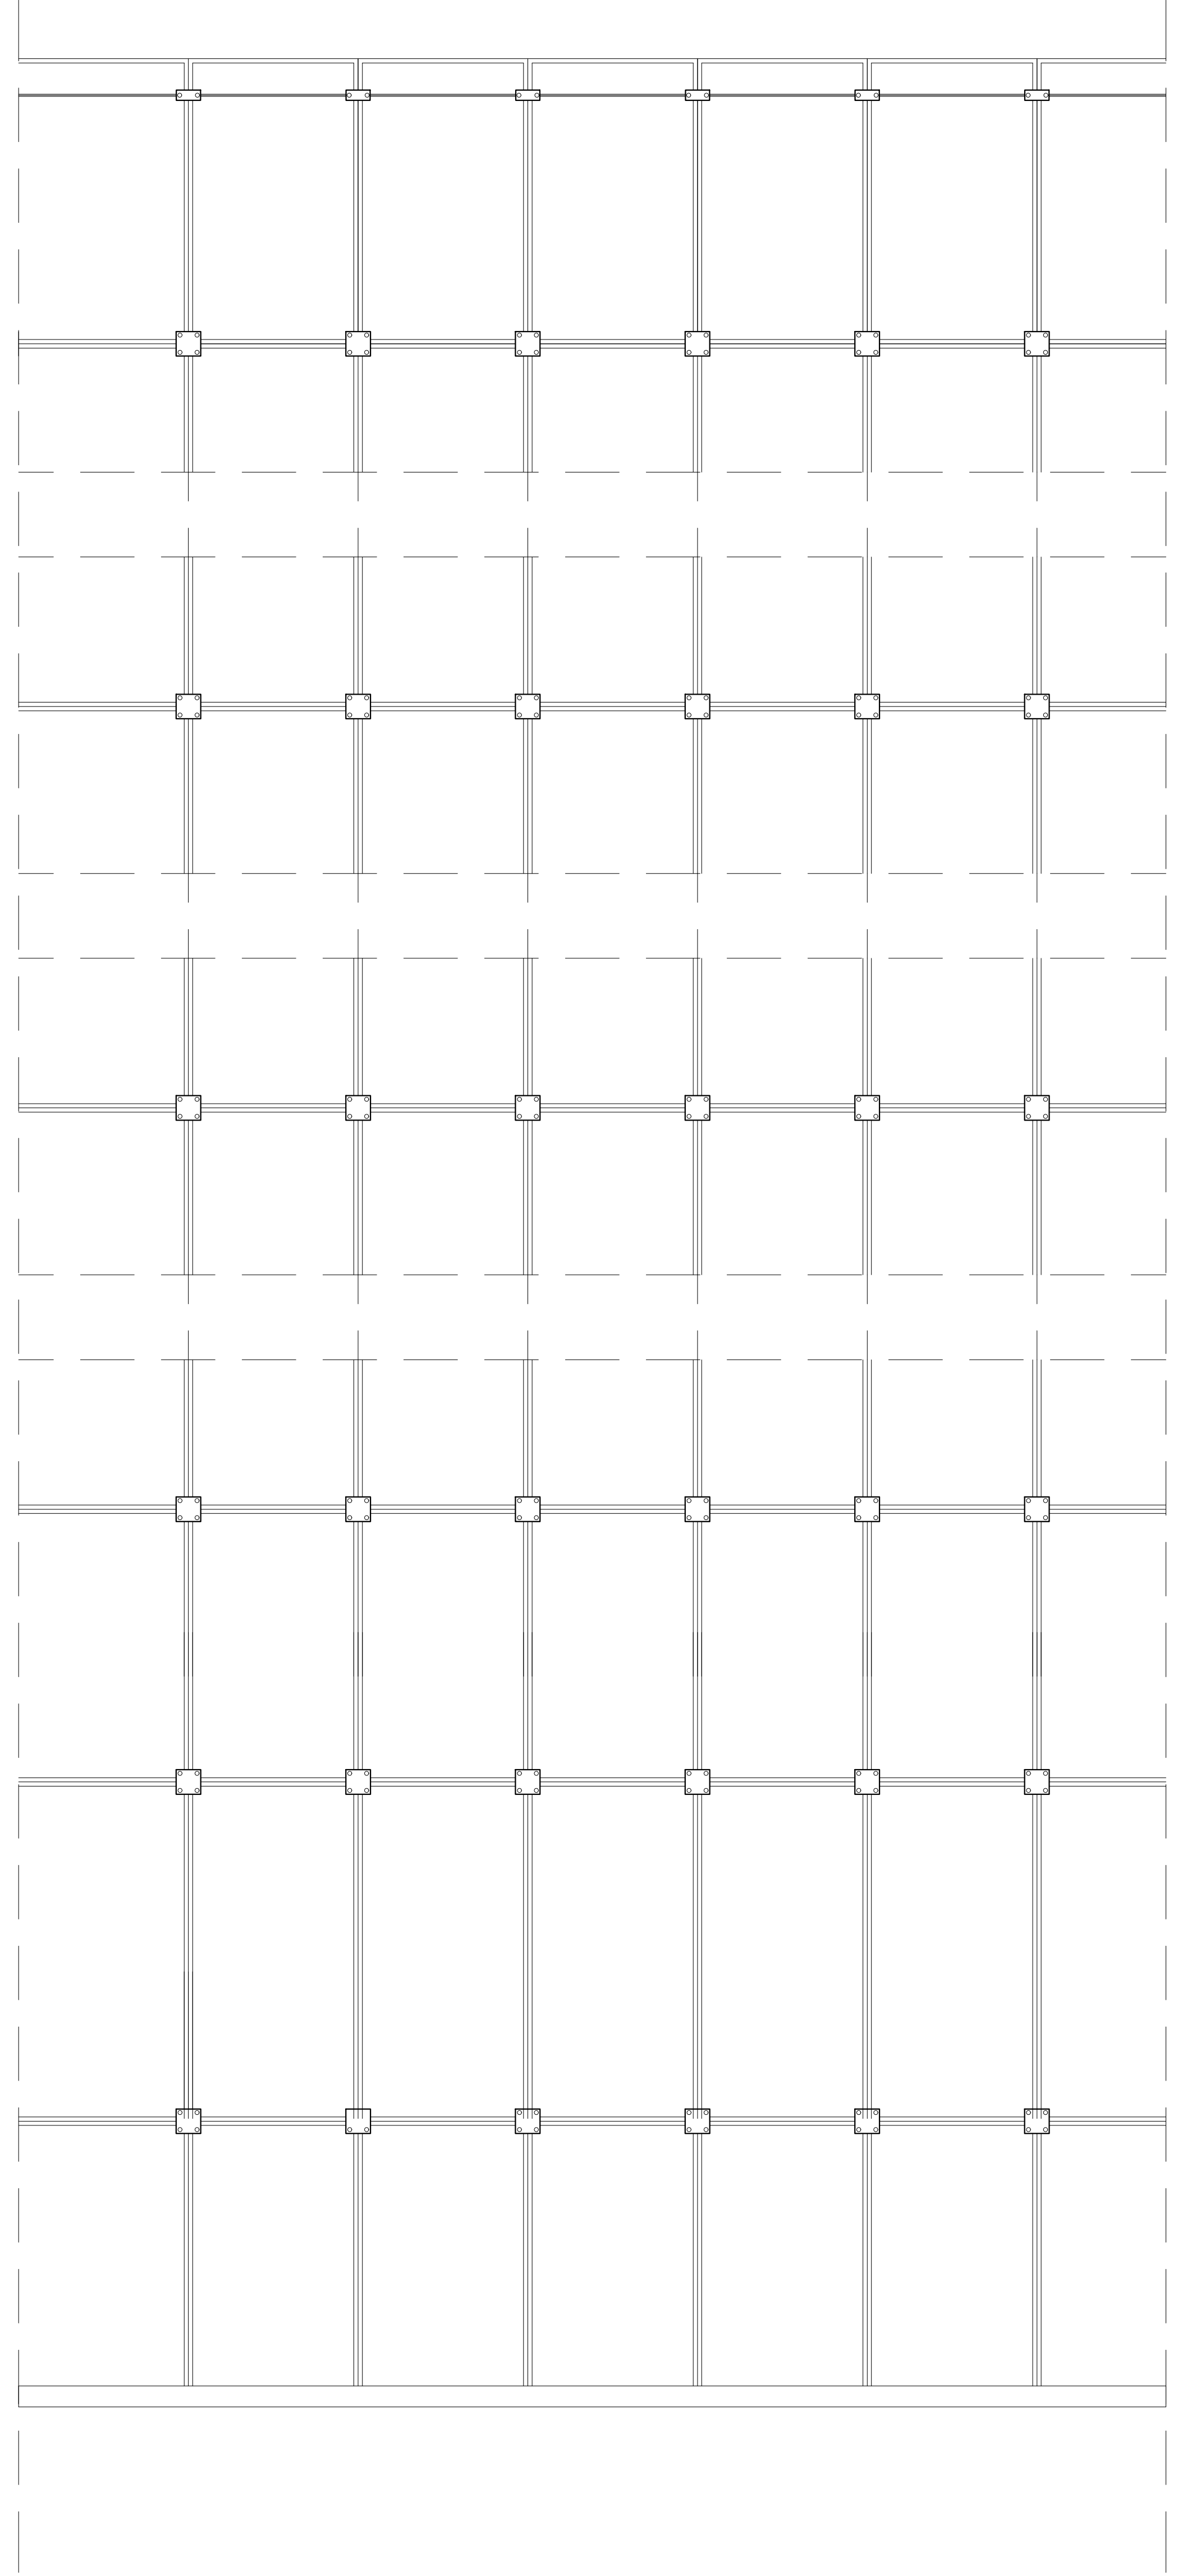


A


A

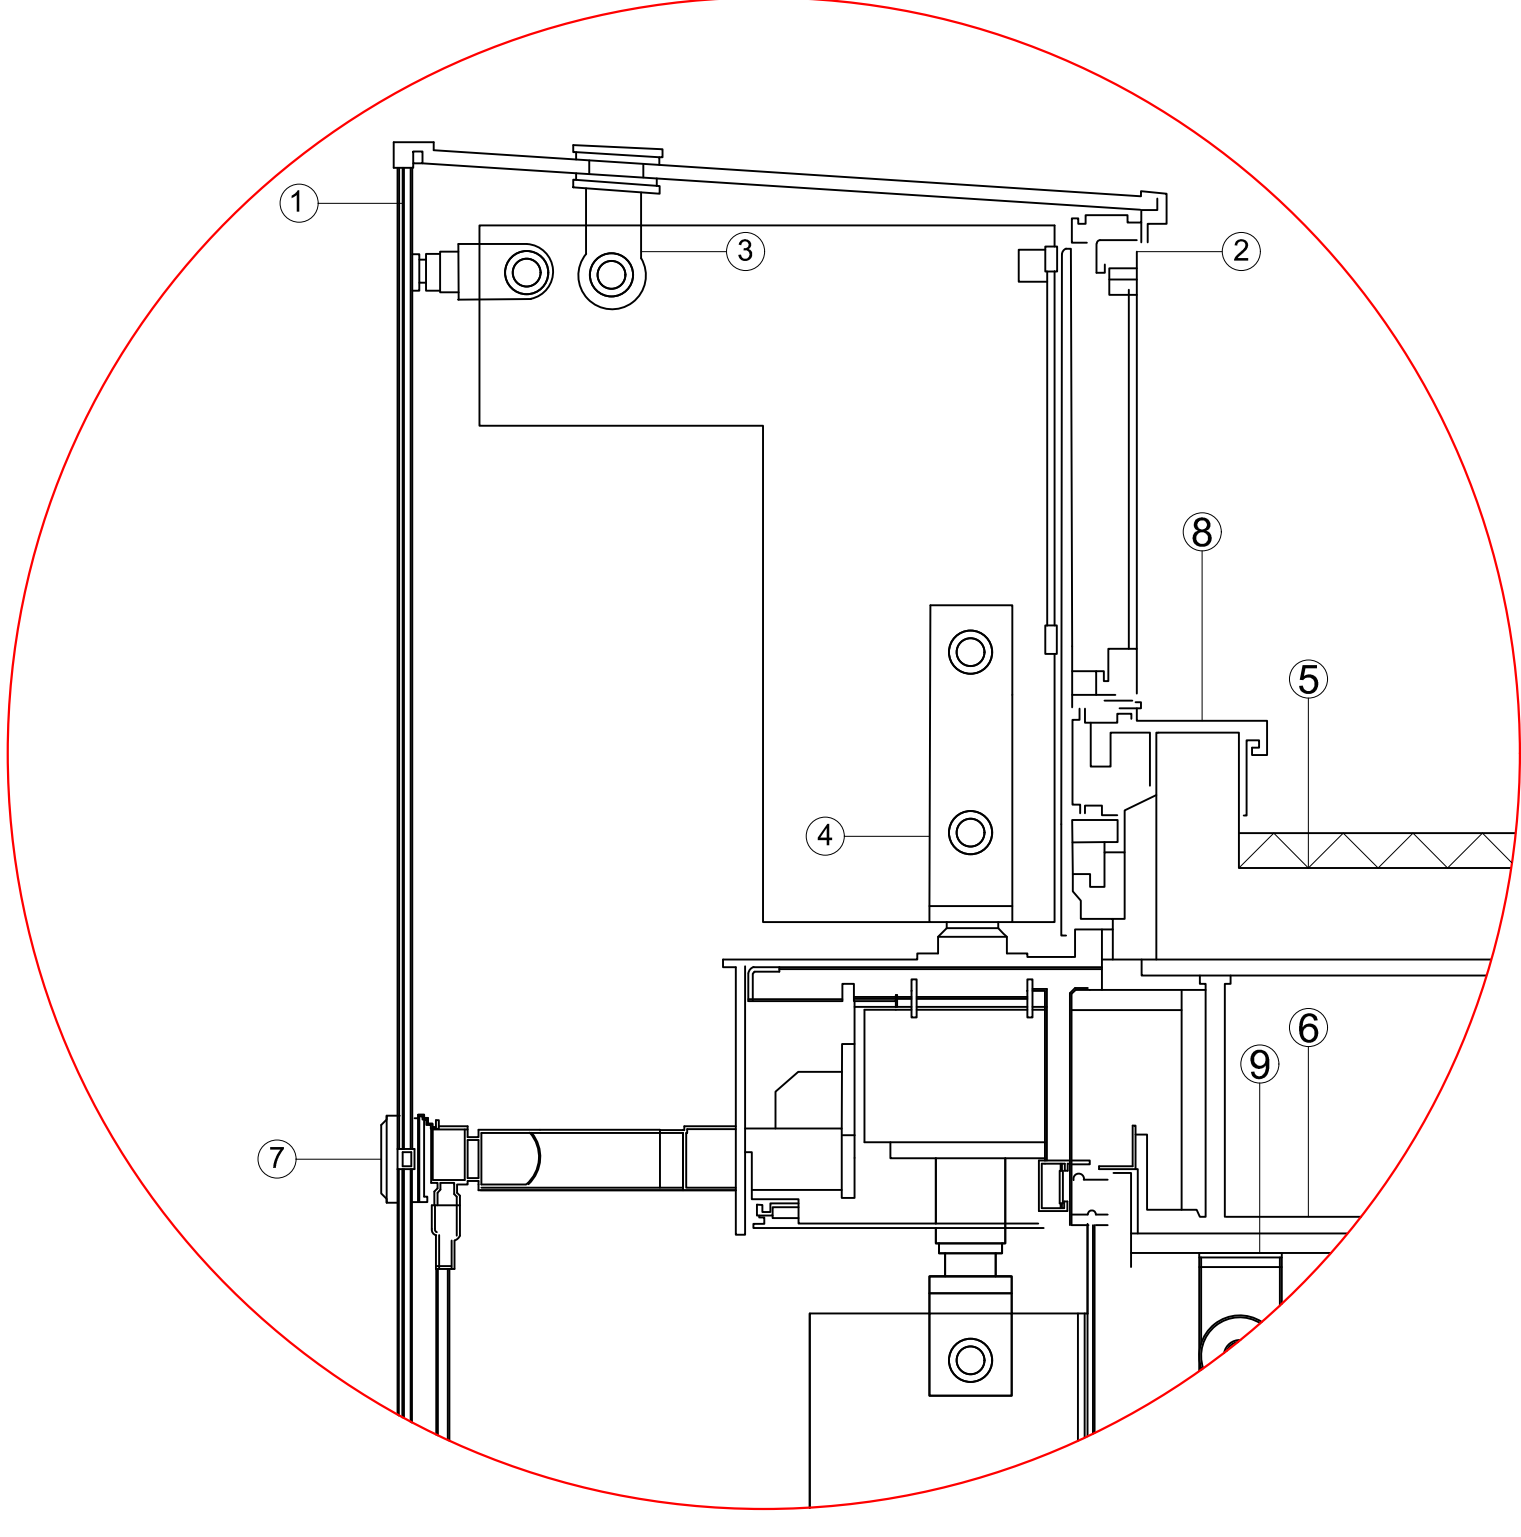


- 1.Temperli camdan oluşan lamine cam kaplama
- 2.Havalandırma için açılır kanat
- 3.Noktasal bağlantı elemanları
- 4.Bağlantı elemanı
- 5.Su yalıtım membranı, ısı yalıtımı,hafif beton
- 6.Hava boşluklu çelik plakalardan oluşan döşeme
- 7.Noktasal bağlantı elemanları
- 8.Alüminyum sac kapak
- 9.Hareketli güneş koruyucu

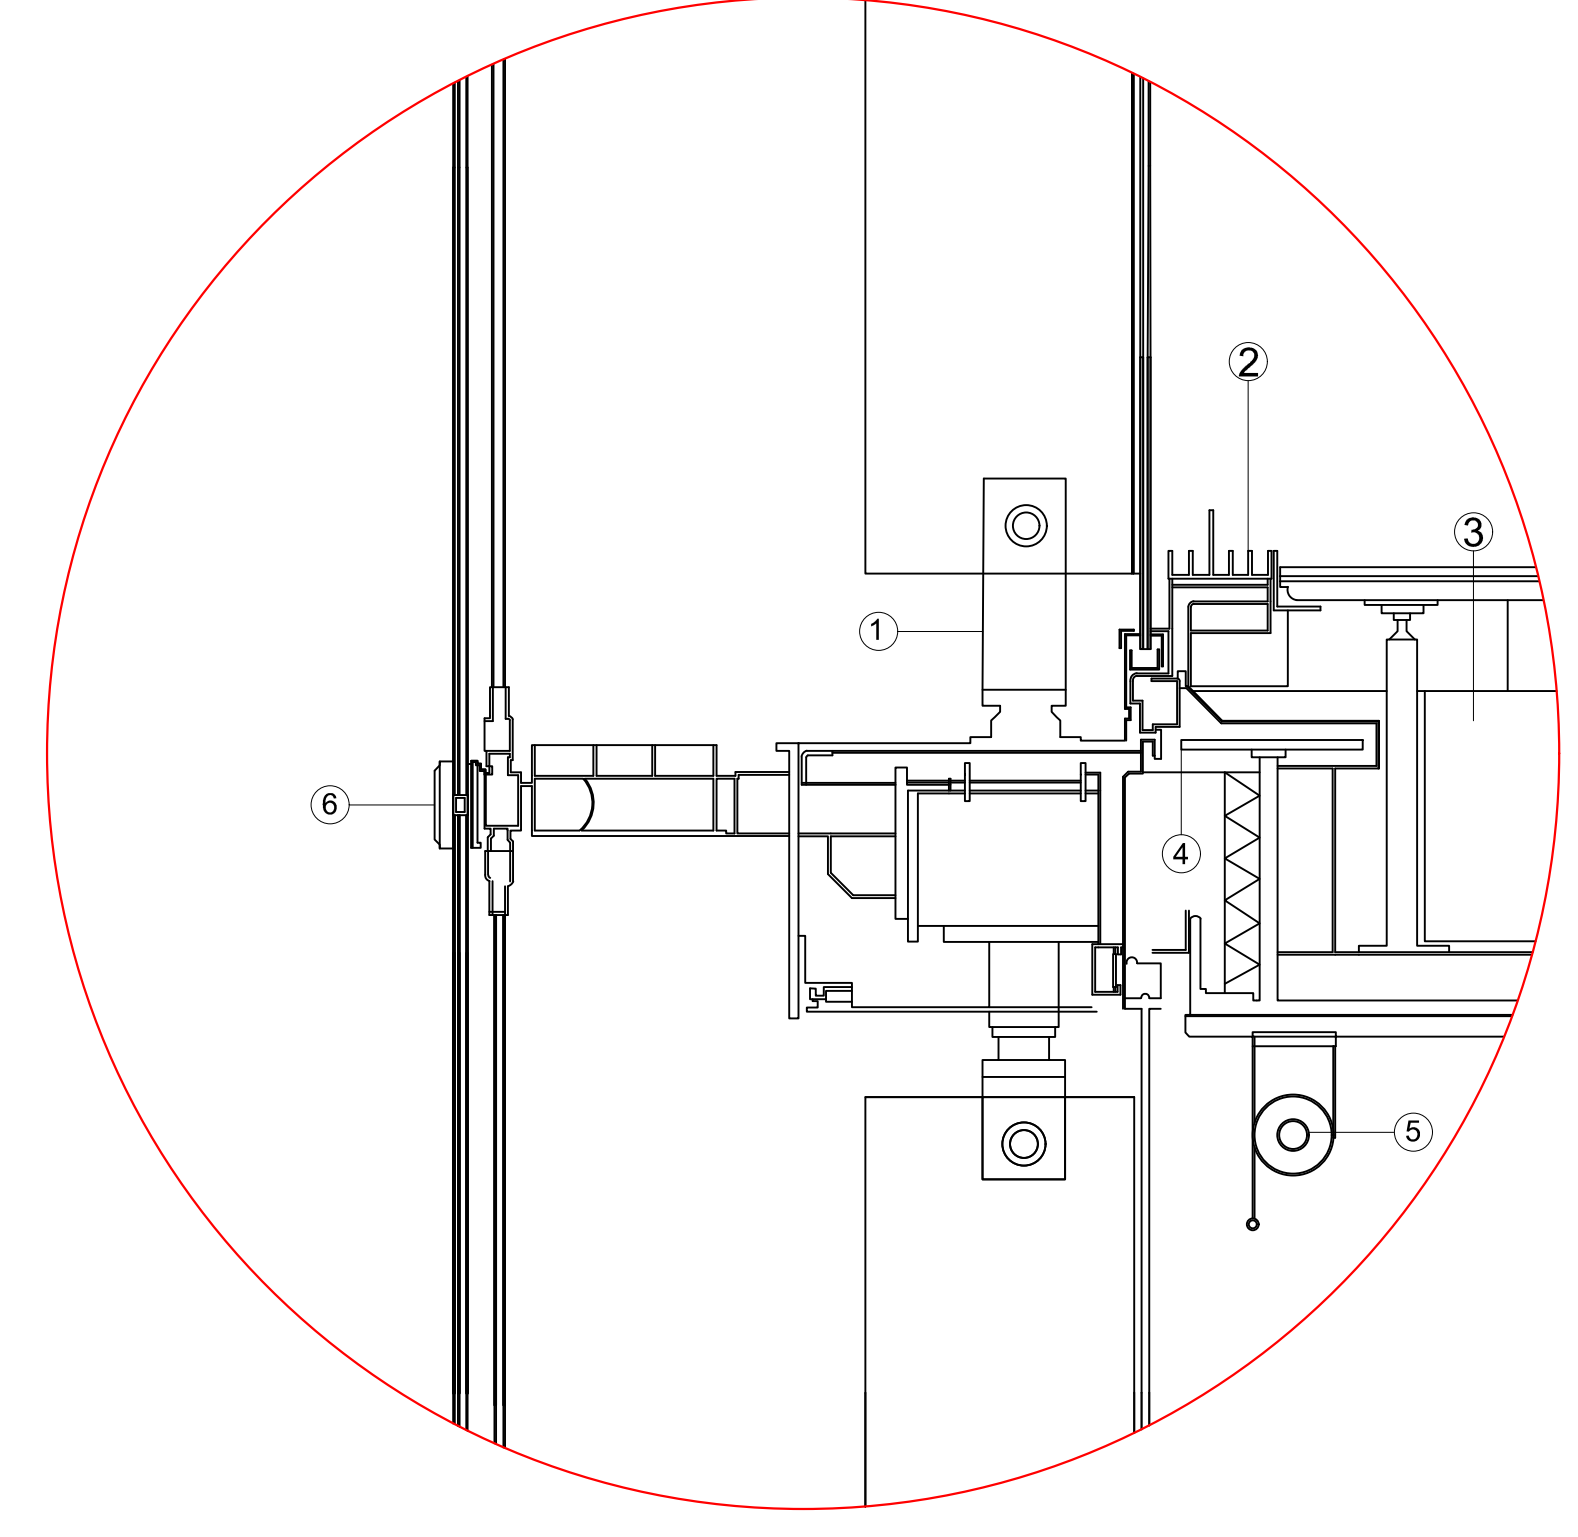

- 1.Noktasal bağlantı elemanı
- 2.Çelik havalandırma ızgarası
- 3.Havalandırma ve ısıtma kanalı
- 4.L çelik köşebent
- 5.Hareketli güneş koruyucu
- 6.Noktasal bağlantı elemanı

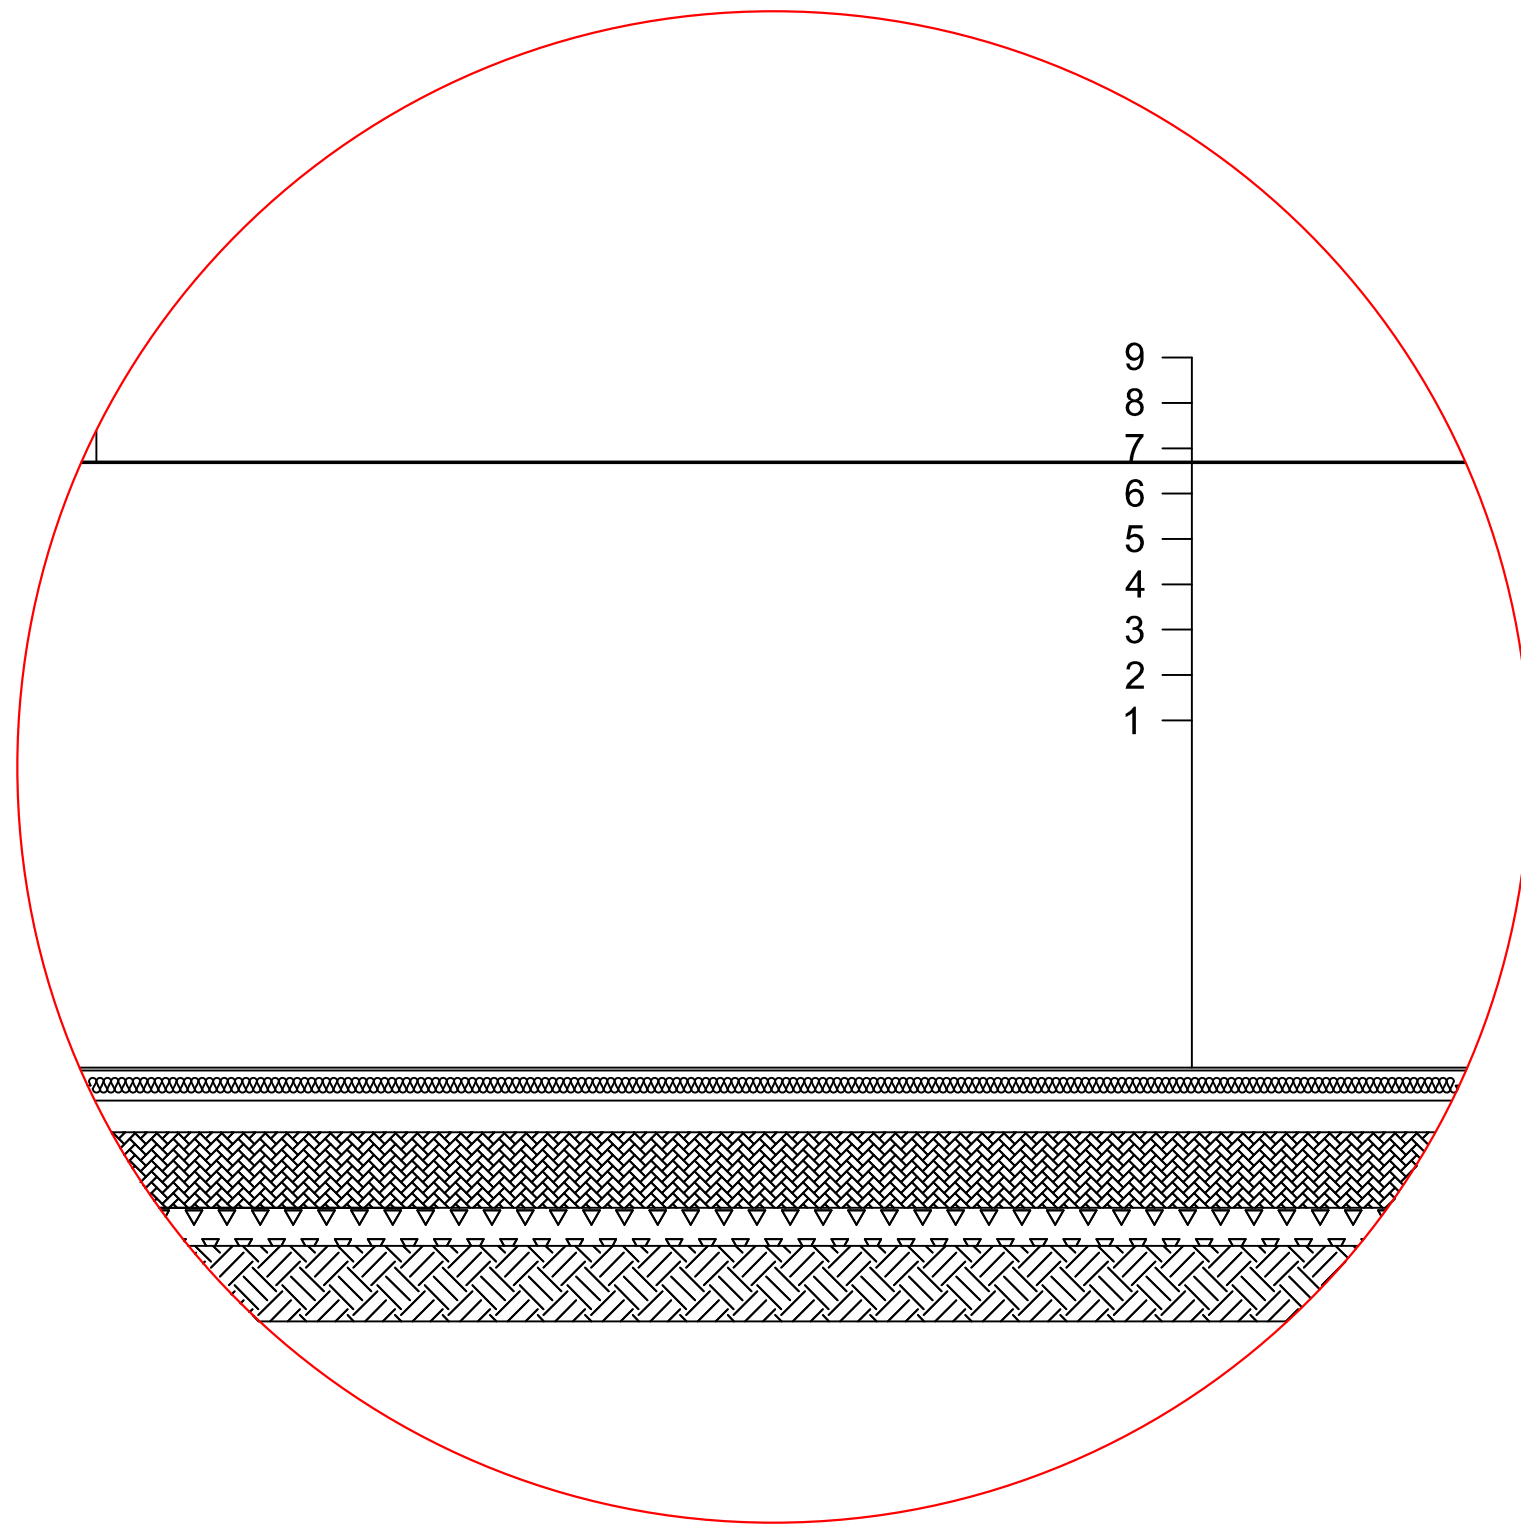

- 1.Sıkıştırılmış toprak
- 2.Blokaj (5CM)
- 3.Grobeton (10CM)
- 4.Koruma betonu (8CM)
- 5.İsı yalıtımı XPS (4CM)
- 6.Radye temel (80CM)
- 7.Epoksi astar (4MM)
- 8.Dolgulu epoksi (1MM)
- 9.Epoksi kaplama (0.5MM)

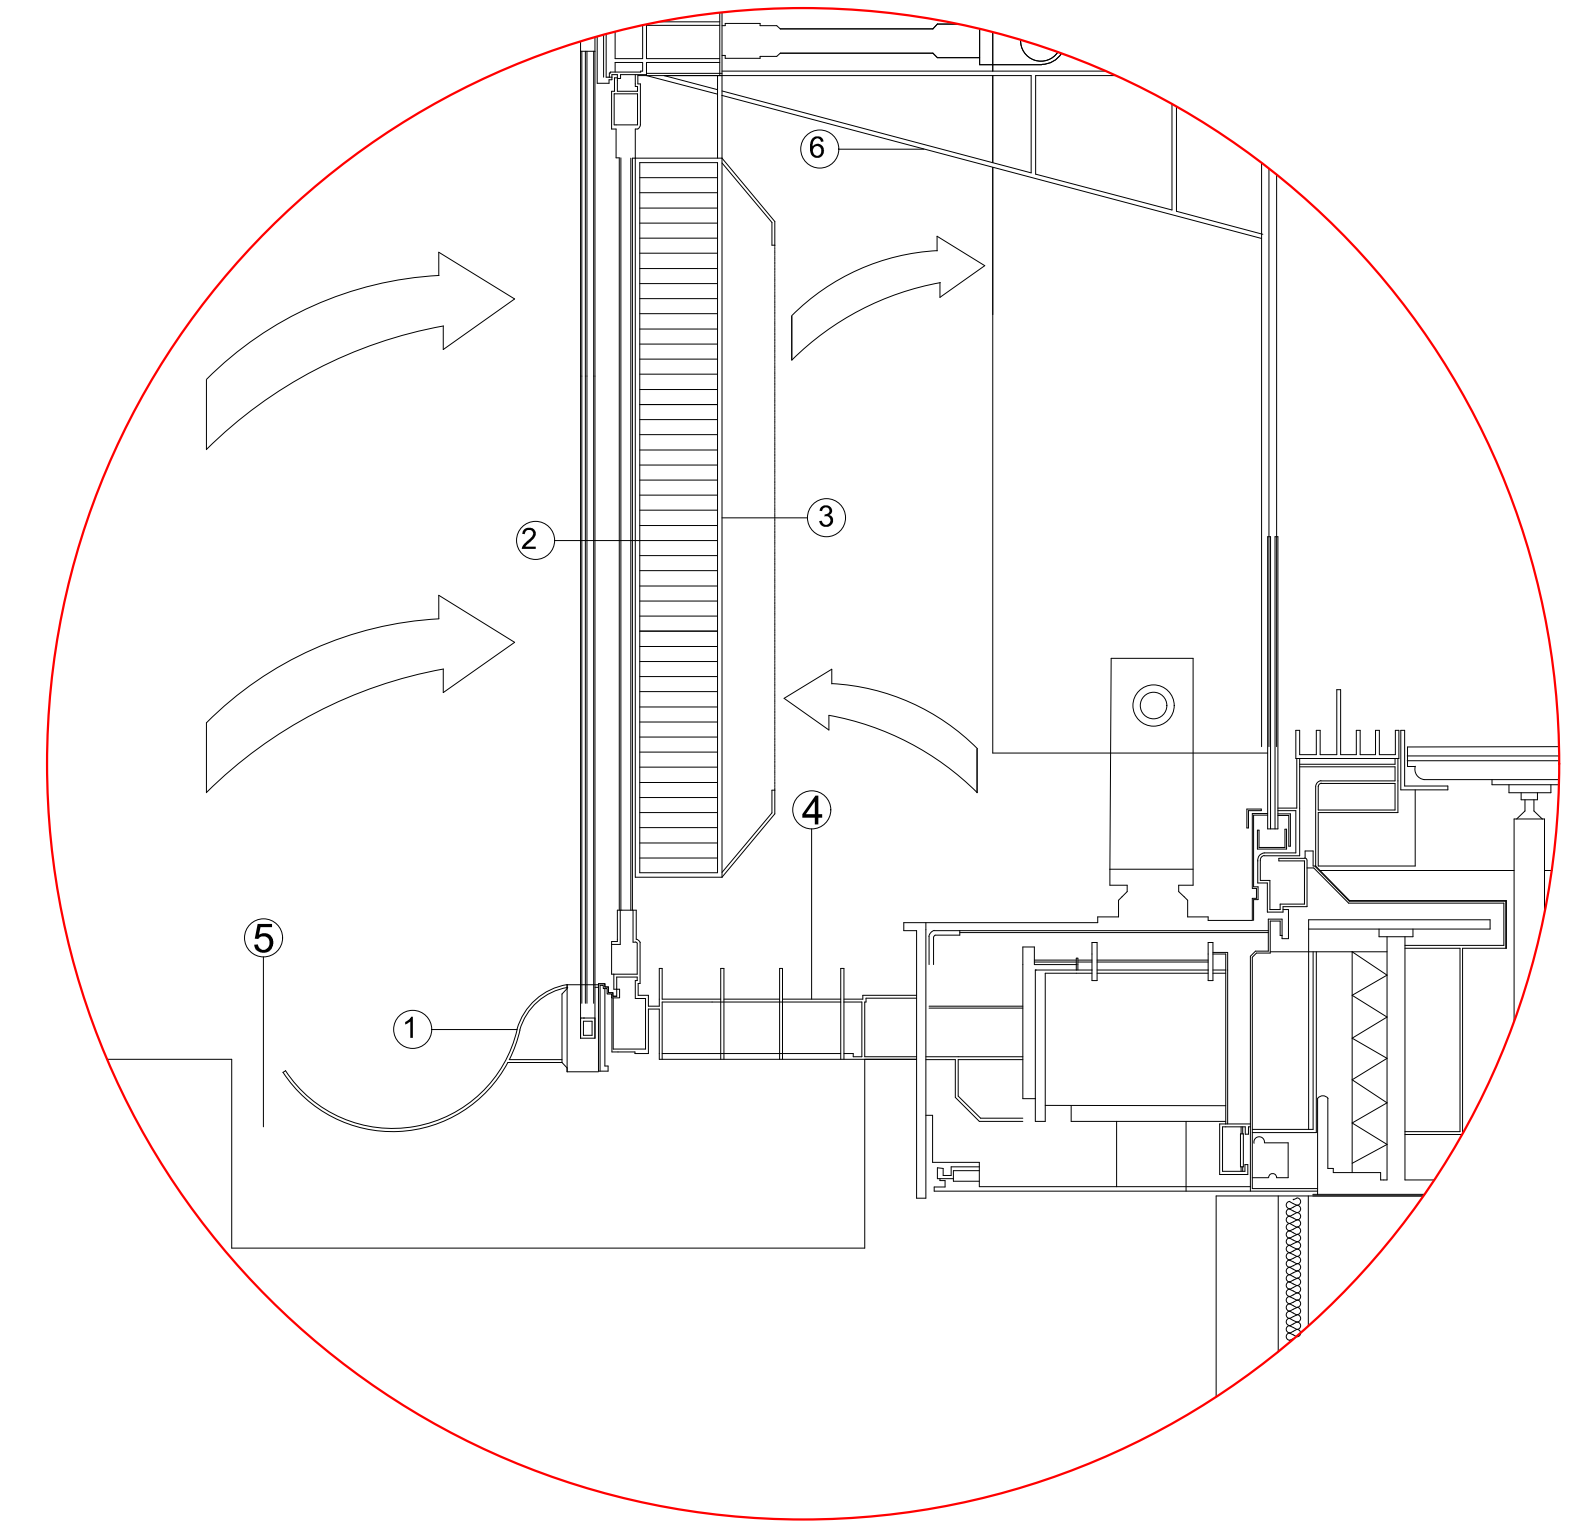

- 1.Hava girişi menfezi
- 2.Hava akışı okları
- 3.Filtre paneli
- 4.Kedi yolu/ Bakım ızgarası
- 5.Drenaj kanalı/ Tahliye borusu
- 6.Aliminyum taşıyıcı profil